



Alcaldía de
Neiva
2024 - 2027

CERTIFICADO PLANO PREDIAL CATASTRAL - CPPC

FOR-GDAPC-12


Versión: 01

Vigente desde:
Febrero 20 de 2025



CPPC - 0509
PLANCHA NOMENCLATURA IGAC: 3231103p

SUBDIRECCIÓN DE GESTIÓN CATASTRAL

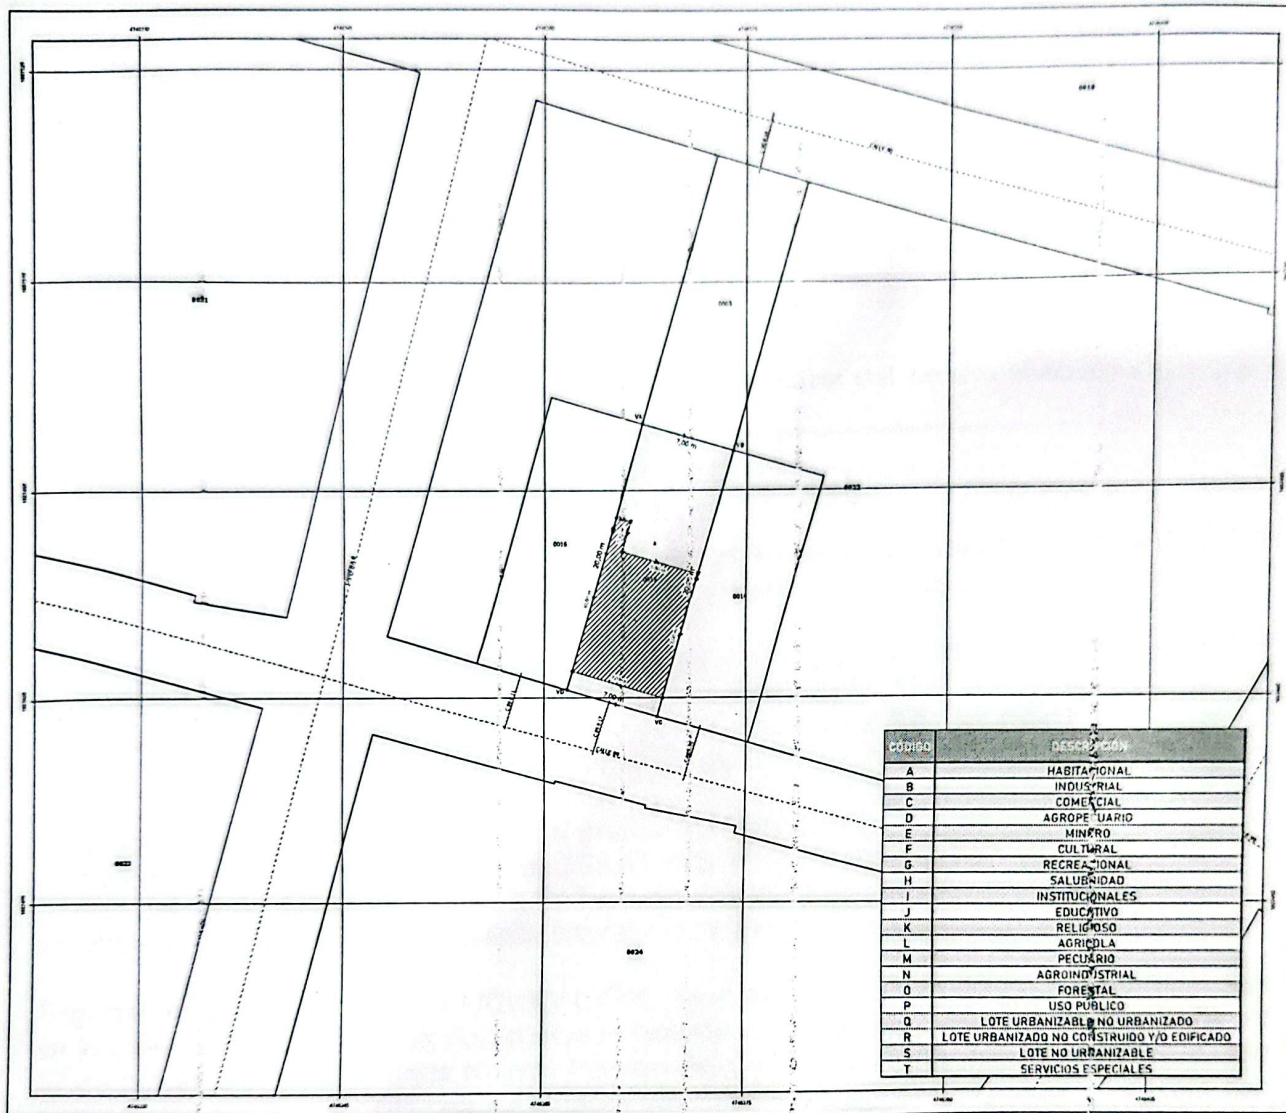

DATOS DEL PREDIO	
NÚMERO PREDIAL (Referencia Catastral que se cita en el recibo de impuesto predial municipal)	010900000220001500000000
NÚMERO PREDIAL ANTERIOR:	010900220015000
NÚMERO PREDIAL NACIONAL - NPM	410010109000000220015000000000
CERTIFICADO DE MATRÍCULA INMOBILIARIA:	NO TIENE
DIRECCIÓN:	C 89 8 17
ÁREA DE TERRENO:	140 m²
ÁREA CONSTRUIDA:	0 m²
NÚMERO ÚNICO PREDIAL -- NUPRE:	NO TIENE
TIPO DE PREDIO:	URBANO

VERTICES	ESTE	NORTE	LADO	LINDERO	LONGITUD (m)
VA	4746367	1887930	VA-VB	410010109000000220003000000000	7,00 m
VB	4746374	1887498	VB-VC	410010109000000220014000000000	20,00 m
VC	4746368	1887479	VC-VD	CALLE 89	7,00 m
VD	4746367	1887130	VD-VA	410010109000000220016000000000:200-63973	20,00 m

SISTEMA DE REFERENCIA
Sistema de Coordenadas: MAGNA-SIRGAS
Proyección: Transversa de Mercator
Elipsoidal: GRS80
Datum: MAGNA
Origen: Latitud: 4° N
Origen: Longitud: 73° W
Falso Este: 5000000
Falso Norte: 2000000
Unidades: Metros
Factor de escala: 0,9992


ESCALA: 1:150
Un (1) centímetro en el mapa equivale a 1,5 metros en terreno

0 4 25 0 8,5 Metros

FUENTE DE INFORMACIÓN
INSTITUTO GEOGRÁFICO AGUSTÍN CODAZZI - IGAC
SUBDIRECCIÓN DE GESTIÓN CATASTRAL - SGC

FECHA: 07 DE OCTUBRE DE 2025
CPPC: 0509

LOCALIZACIÓN PREDIO

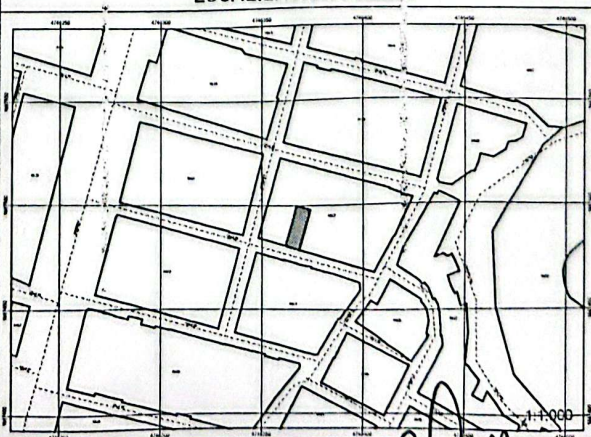

CONVENCIONES

URBANO	RURAL
Vertice	1 nomenclatura dominante
Zone de estudio	1 nomenclatura vial
1 nomenclatura dominante	1 nomenclatura
1 nomenclatura secundaria	1 nomenclatura
1 nomenclatura vial	1 nomenclatura
1 terreno	1 terreno
1 manzana	1 sector
1 construcción	1 patrimonio
1 nomenclatura	
1 patrimonio	
1 sector	

OFICINA DE GESTIÓN CATASTRAL
SUBDIRECCIÓN DE GESTIÓN CATASTRAL - SGC
Departamento Administrativo de Planeación - DAP
Msc. GISEL CAJALIN - OFICINARIO MARTÍNEZ FALLA
Profesional Especializado
Subdirección de Gestión Catastral - SGC
Creador del Mapa: MARIA TERESA COMBES LINDER
Profesional - Catastrista
Subdirección de Gestión Catastral - SGC

NOTA: EL PRESENTE CERTIFICADO SE EXPIDE ÚNICAMENTE CON FINES CATASTRALES Y NO ES VÁLIDA PARA ACLARAR O MODIFICAR ÁREA Y/O LINDEROS SEGÚN RESOLUCIÓN CONJUNTA IGAC No. 1101, SNR No. 11344 DEL 31/12/2020.