



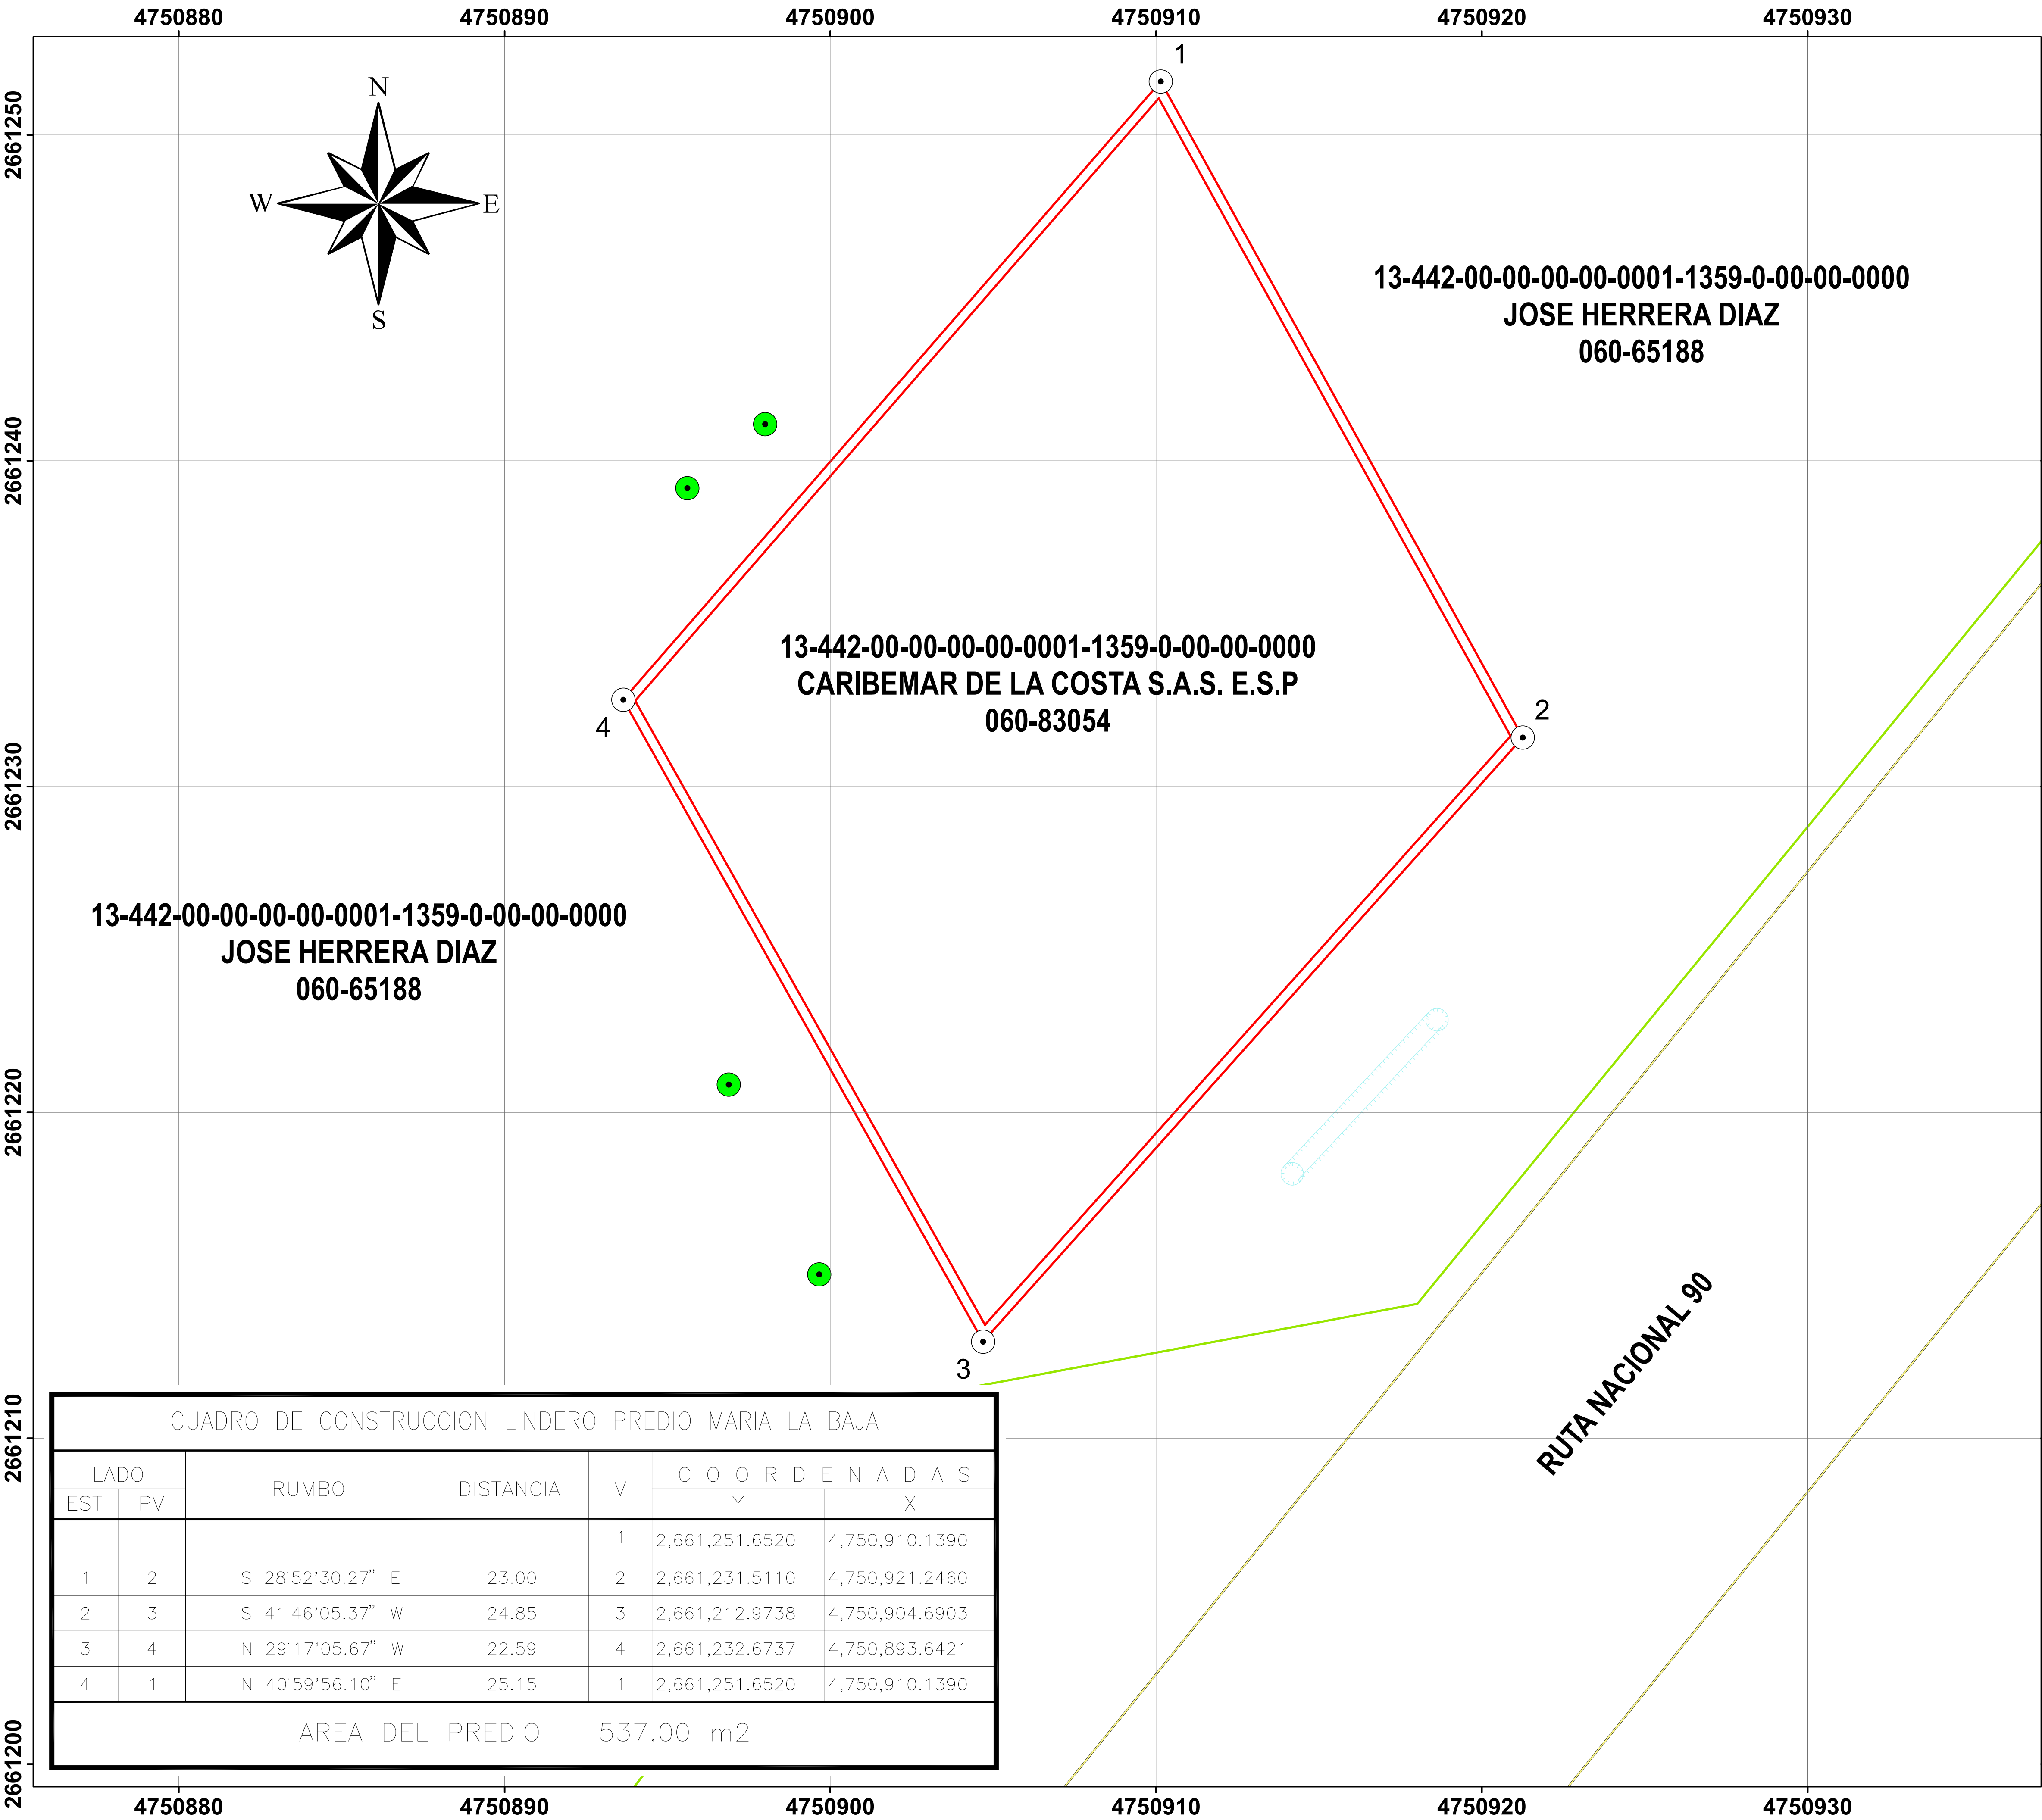

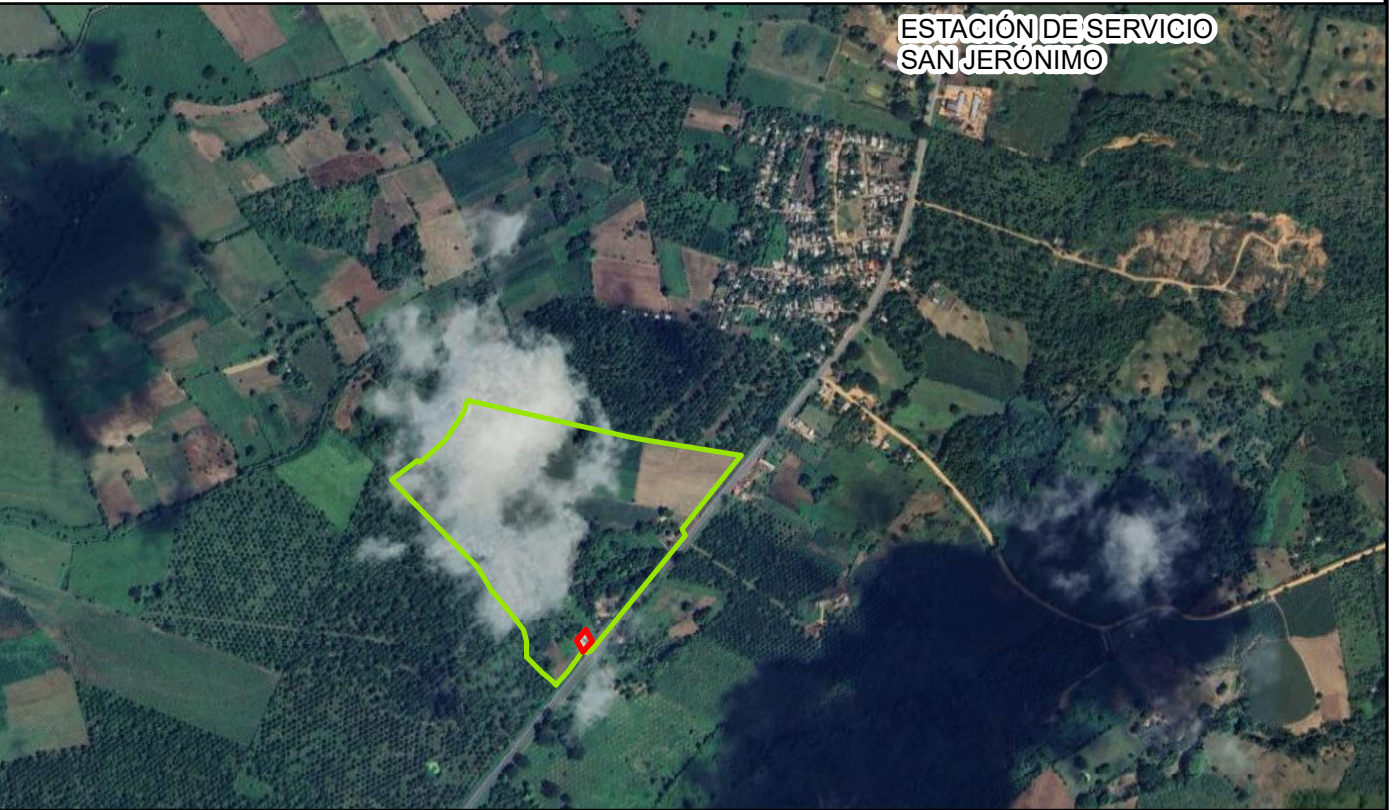

PROYECTO

Levantamiento Topográfico para la gestión predial integral en la constitución de predios requeridos en los diferentes proyectos adelantados por AFINIA grupo EPM

NOMBRE DEL PREDIO

SC MARQUEZ LT DE TERRENO DENOMINADO LA UNION

CODIGO PREDIAL NUEVO

13-442-00-00-00-00-0001-1359-0-00-00-0000

CODIGO PREDIAL ANTERIOR	FOLIO DE MATRICULA
1344200000001A627000	060-83054

PROPIETARIO(Registro)

CARIBEMAR DE LA COSTA S.A.S. E.S.P

ÁREA TOTAL DEL PREDIO	537.000 m2
-----------------------	------------

OBJETO

El contrato 4126000036 de 2026 suscrito con AFINIA Grupo EPM orientado a prestación de servicios de avalúo, topografía y georreferenciación de inmuebles y servidumbres requeridos para las diversas gestiones o tramites que efectúe AFINIA Grupo EPM.

FECHA

28/05/2026

REVISÓ	ELABORÓ
AFINIA grupo EPM	Paula María Rincón González Licencia No. 01-18135

ESCALA	N°PLANO	REVISO
1:100	1/1	Juan Gabriel García Villanueva Licencia No. 25335-343295 CND

CONVENCIONES

- Vértices_Lindero
- Lindero
- Poste
- Vía
- Cuneta
- Predio Mayor Extension

ESCALA GRAFICA

5 2.5 0 5 Meters

SISTEMA DE REFERENCIA

Coordinate System: MAGNA-SIRGAS Origen-Nacional
Projection: Transverse Mercator
Datum: MAGNA
False Easting: 5 000 000.0000
False Northing: 2 000 000.0000
Central Meridian: -73.0000
Scale Factor: 0.9992
Latitude Of Origin: 4.0000
Units: Meter