


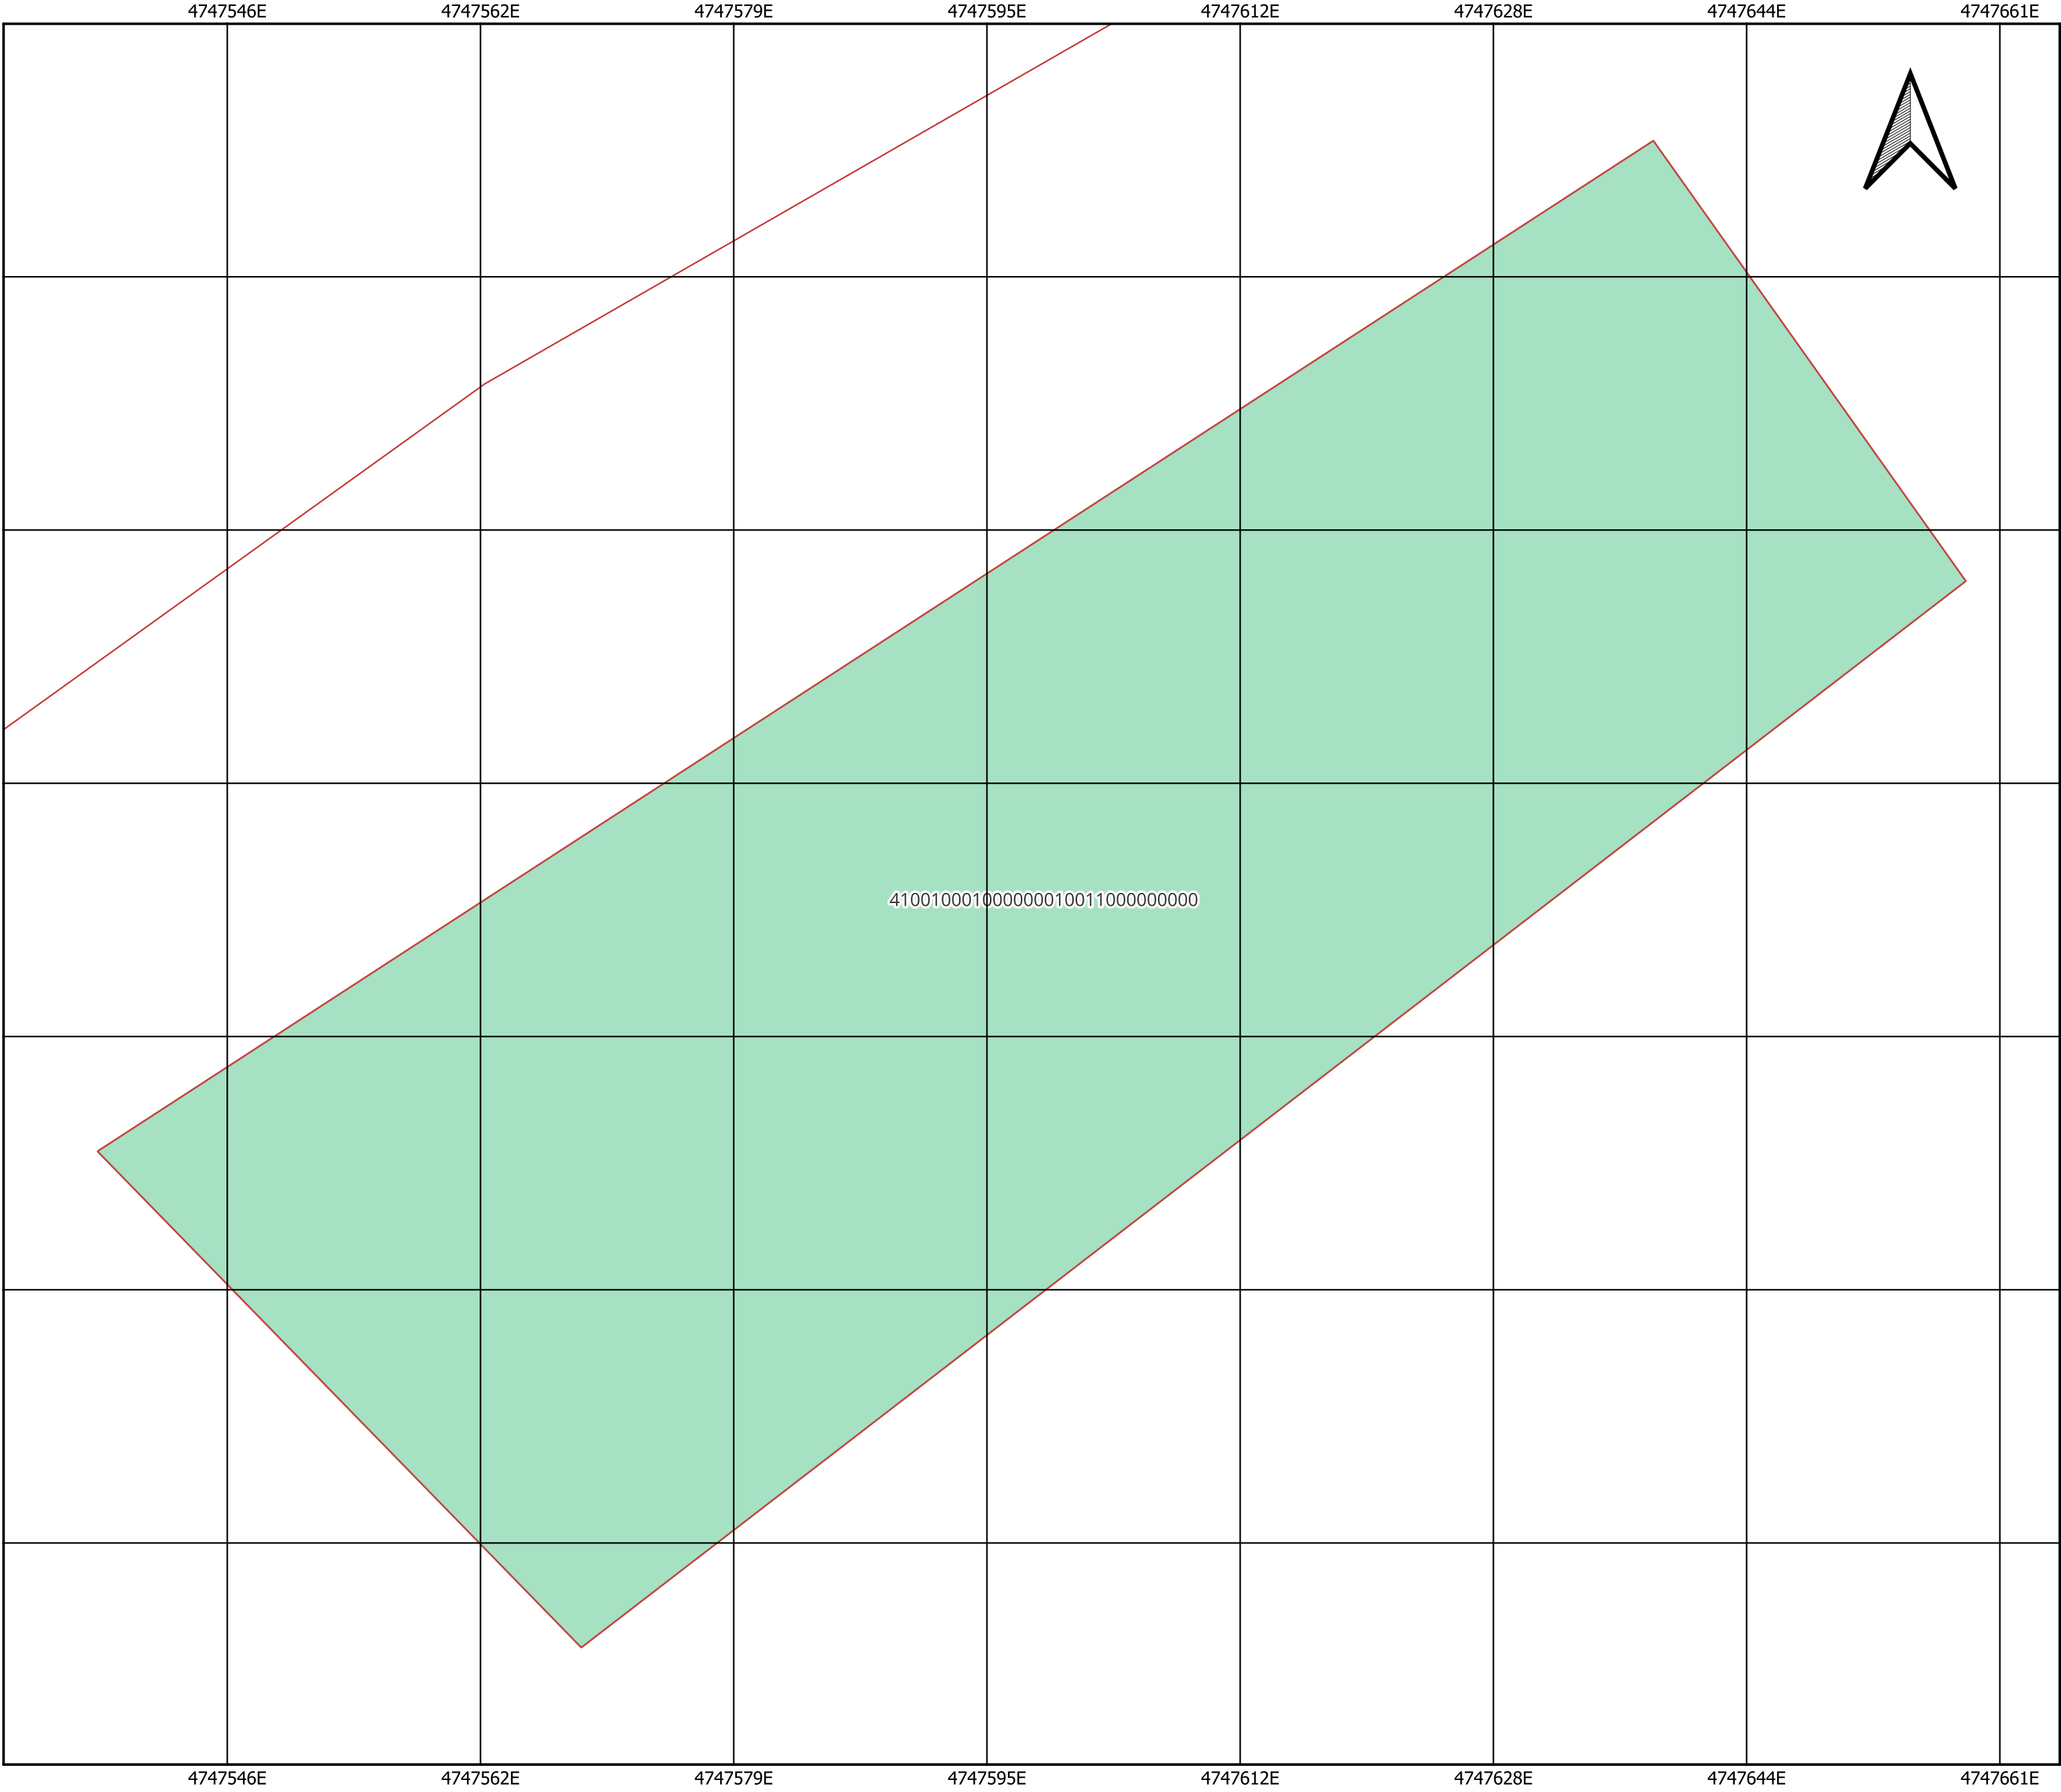

Alcaldía de
Neiva

FOR -GDAPC -11

VERSION: 1

VIGENTE DESDE:
Noviembre 09 de 2025

CCU-CARTA CATASTRAL URBANA-MANZANA
SUBDIRECCIÓN DE GESTIÓN CATASTRAL

CARTA CATASTRAL URBANA

UBICACIÓN CATASTRAL:

DEPARTAMENTO:	41
MUNICIPIO:	001
ZONA:	00
SECTOR:	01
COMUNA:	00
BARRIO:	00
MANZANA:	0001
TERRENO:	0011
CONDICION DE PROPIEDAD:	0
NUMERO DEL EDIFICIO O TORRE:	00
NUMERO DEL PISO DENTRO DEL EDIFICIO O TORRE:	00
NUMERO DE LA UNIDAD EN PH, CONDOMINIO O MEJORA:	0000
NÚMERO PREDIAL NACIONAL - NPN:	410010001000000010011000000000

CONVENCIONES

Vertices_0008

Linderos_0008

E_Terreno

Predio

otros

Construccion

Unidad de Construccion

Predios — PREDIOS

Google Satellite

PLANCHA NOMENCLATURA IGAC:

MAPA UBICACIÓN

DATOS DE INFORMACIÓN ESPACIAL:

Sistema de coordenadas: MAGNA-SIRGAS 2018 / Origen-Nacional
Proyeccion: Transverse Mercator
Elipsoide: EPSG:7019
Datúm: MAGNA
Origen: Latitud: 4° N
Origen: Longitud:-73° W
Falso Este:5000000
Falso Norte:2000000
Unidades: metros
Factor de escala: 329.0084717815934

ESCALA:1:329
Un centimetro (1) en el mapa equivale a 329 metros

0

10

20 m

Nota: Derechos reservados. Para la reproducción parcial o total de la presente obra se requiere la previa autorización de la Subdirección de Gestión catastral SGC, el texto, la cartografía y gráficos están sujetos a derechos de copia y de propiedad intelectual (Ley 23 de 1982).

FUENTE DE INFORMACION:

CCU:

FECHA: